


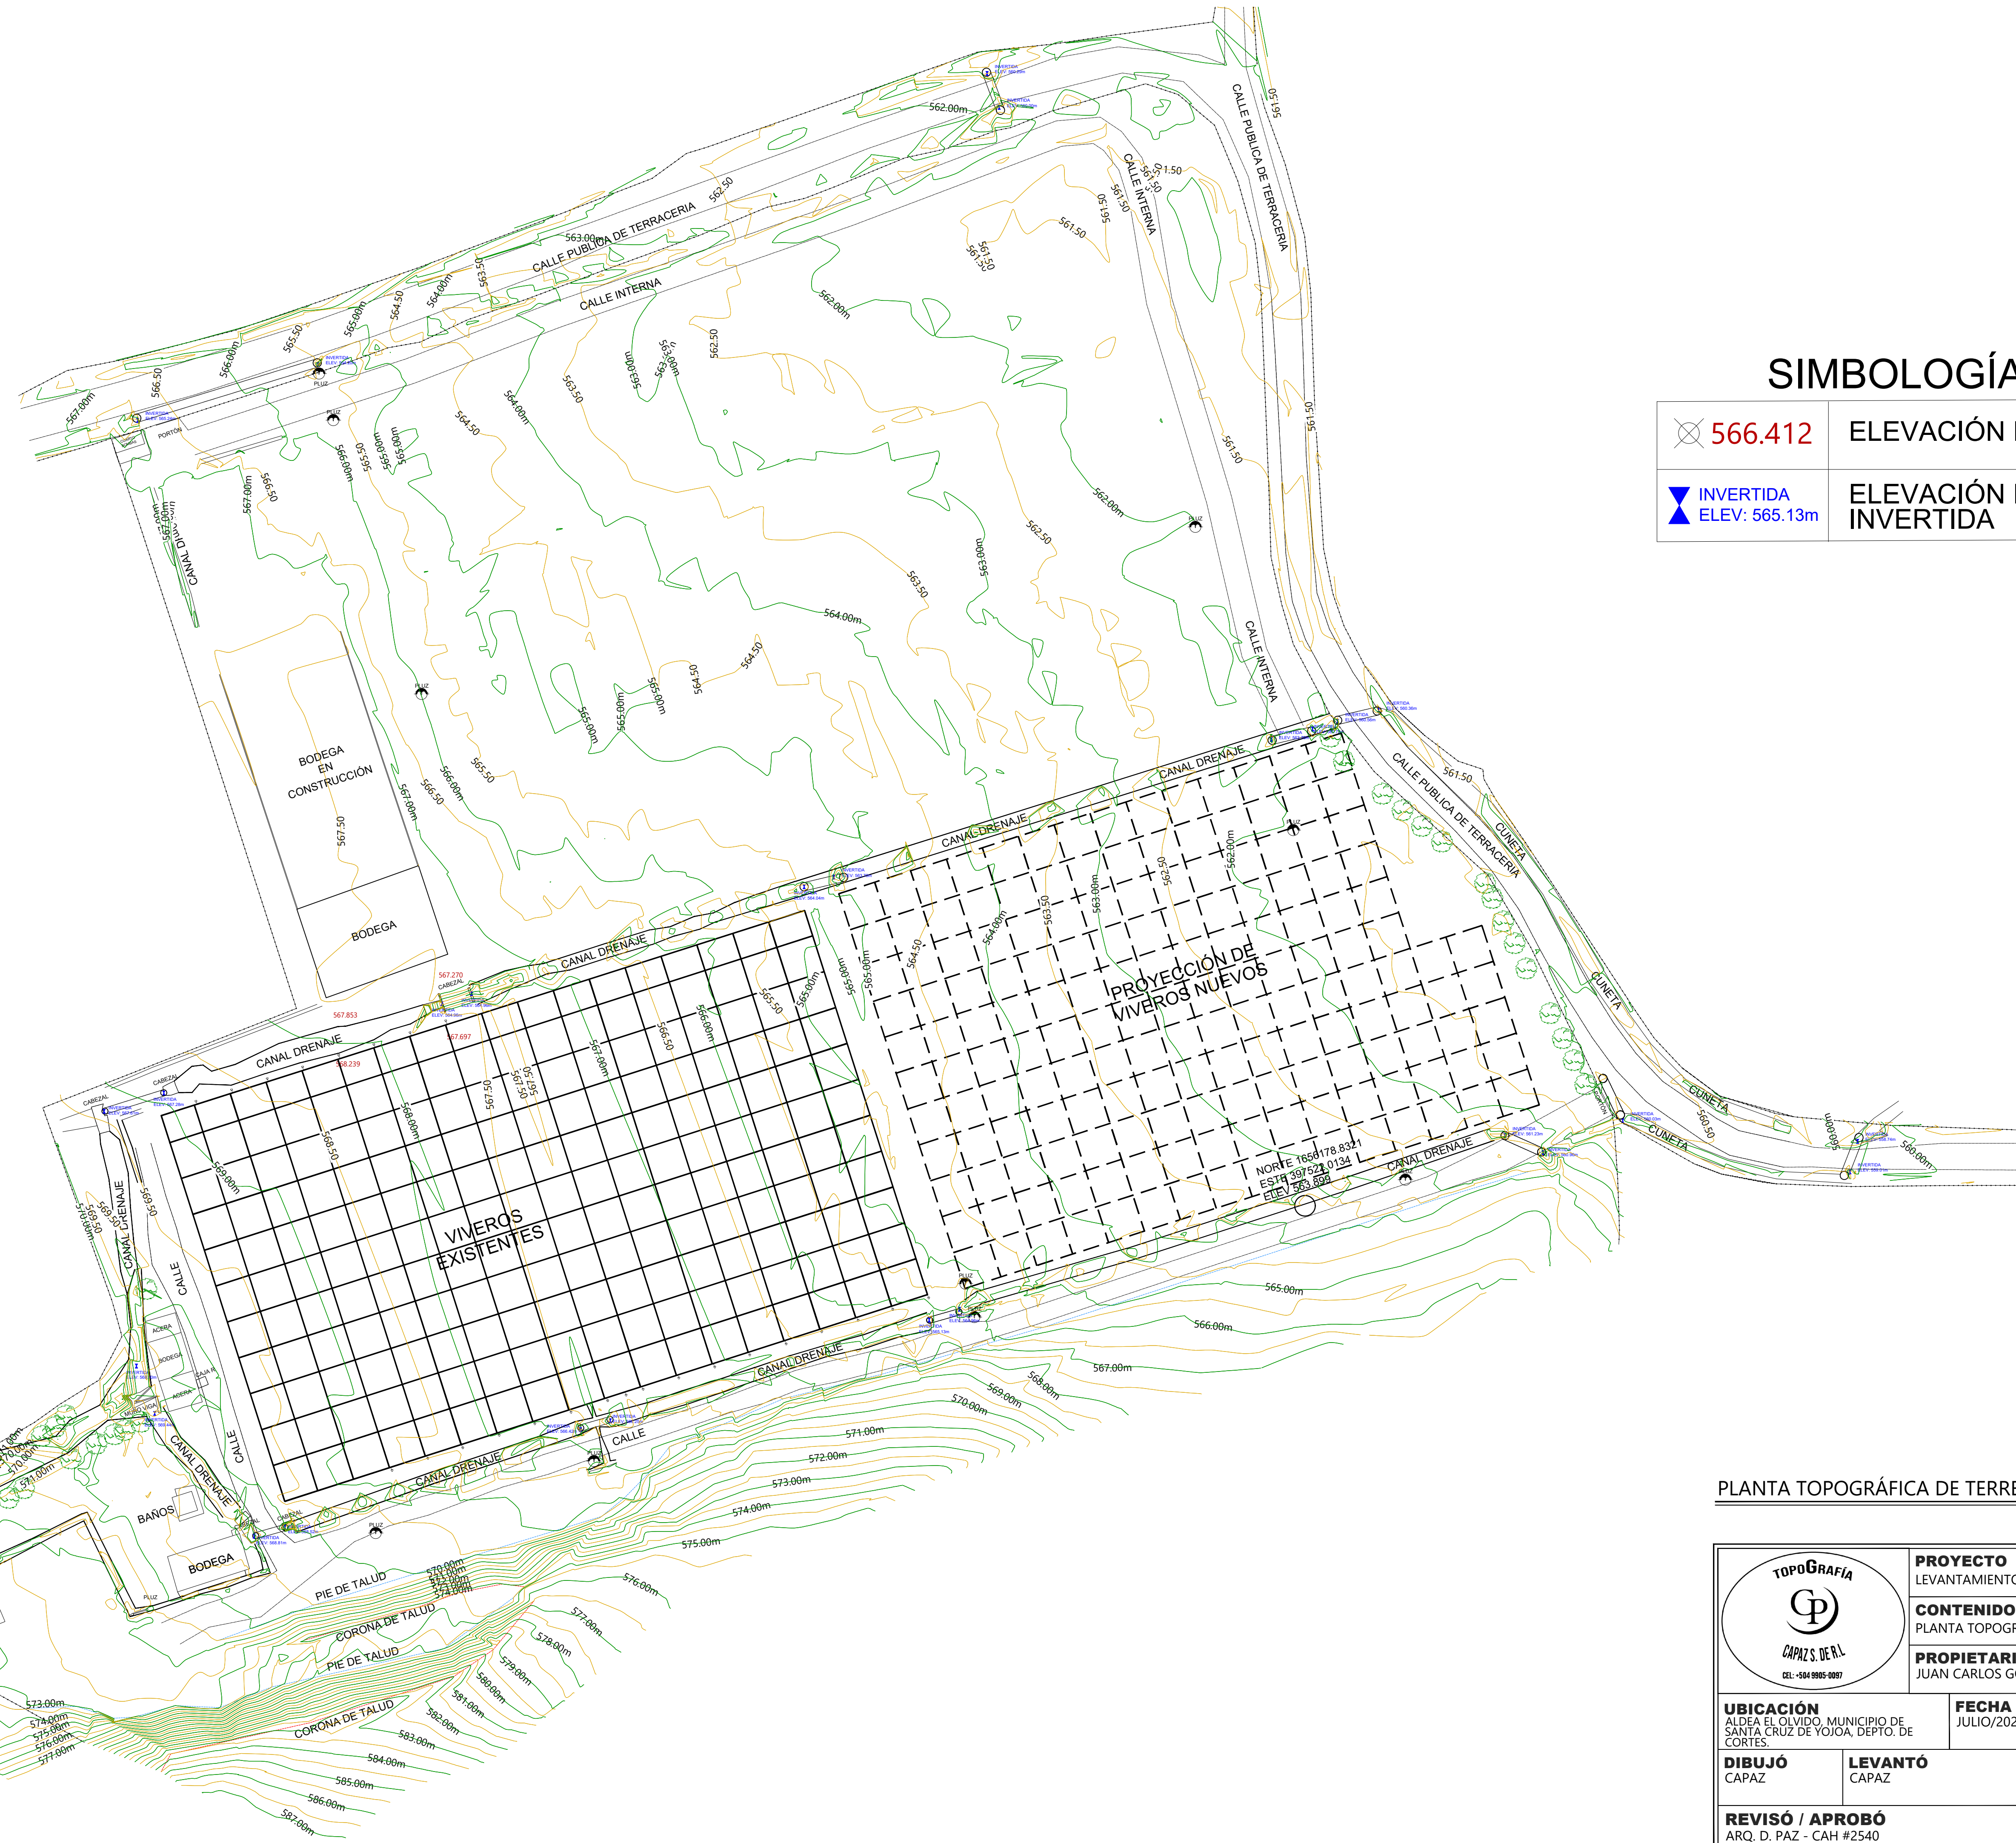

566.412	ELEVACIÓN DE TN
INVERTIDA ELEV: 565.13m	ELEVACIÓN DE INVERTIDA

ESC. 1:830

	PROYECTO LEVANTAMIENTO TOPOGRÁFICO	
	CONTENIDO PLANTA TOPOGRÁFICA DE TERRENO	
PROPIETARIO JUAN CARLOS GONZALES		
UBICACIÓN ALDEA EL OLVIDO, MUNICIPIO DE SANTA CRUZ DE YJOJA, DEPTO. DE CORTÉS	FECHA JULIO/2025	ESCALA 1:1000
DIBUJÓ CAPAZ	LEVANTÓ CAPAZ	# HOJA 01/01
REVISÓ / APROBÓ ARQ. D. PAZ - CAH #2540		